




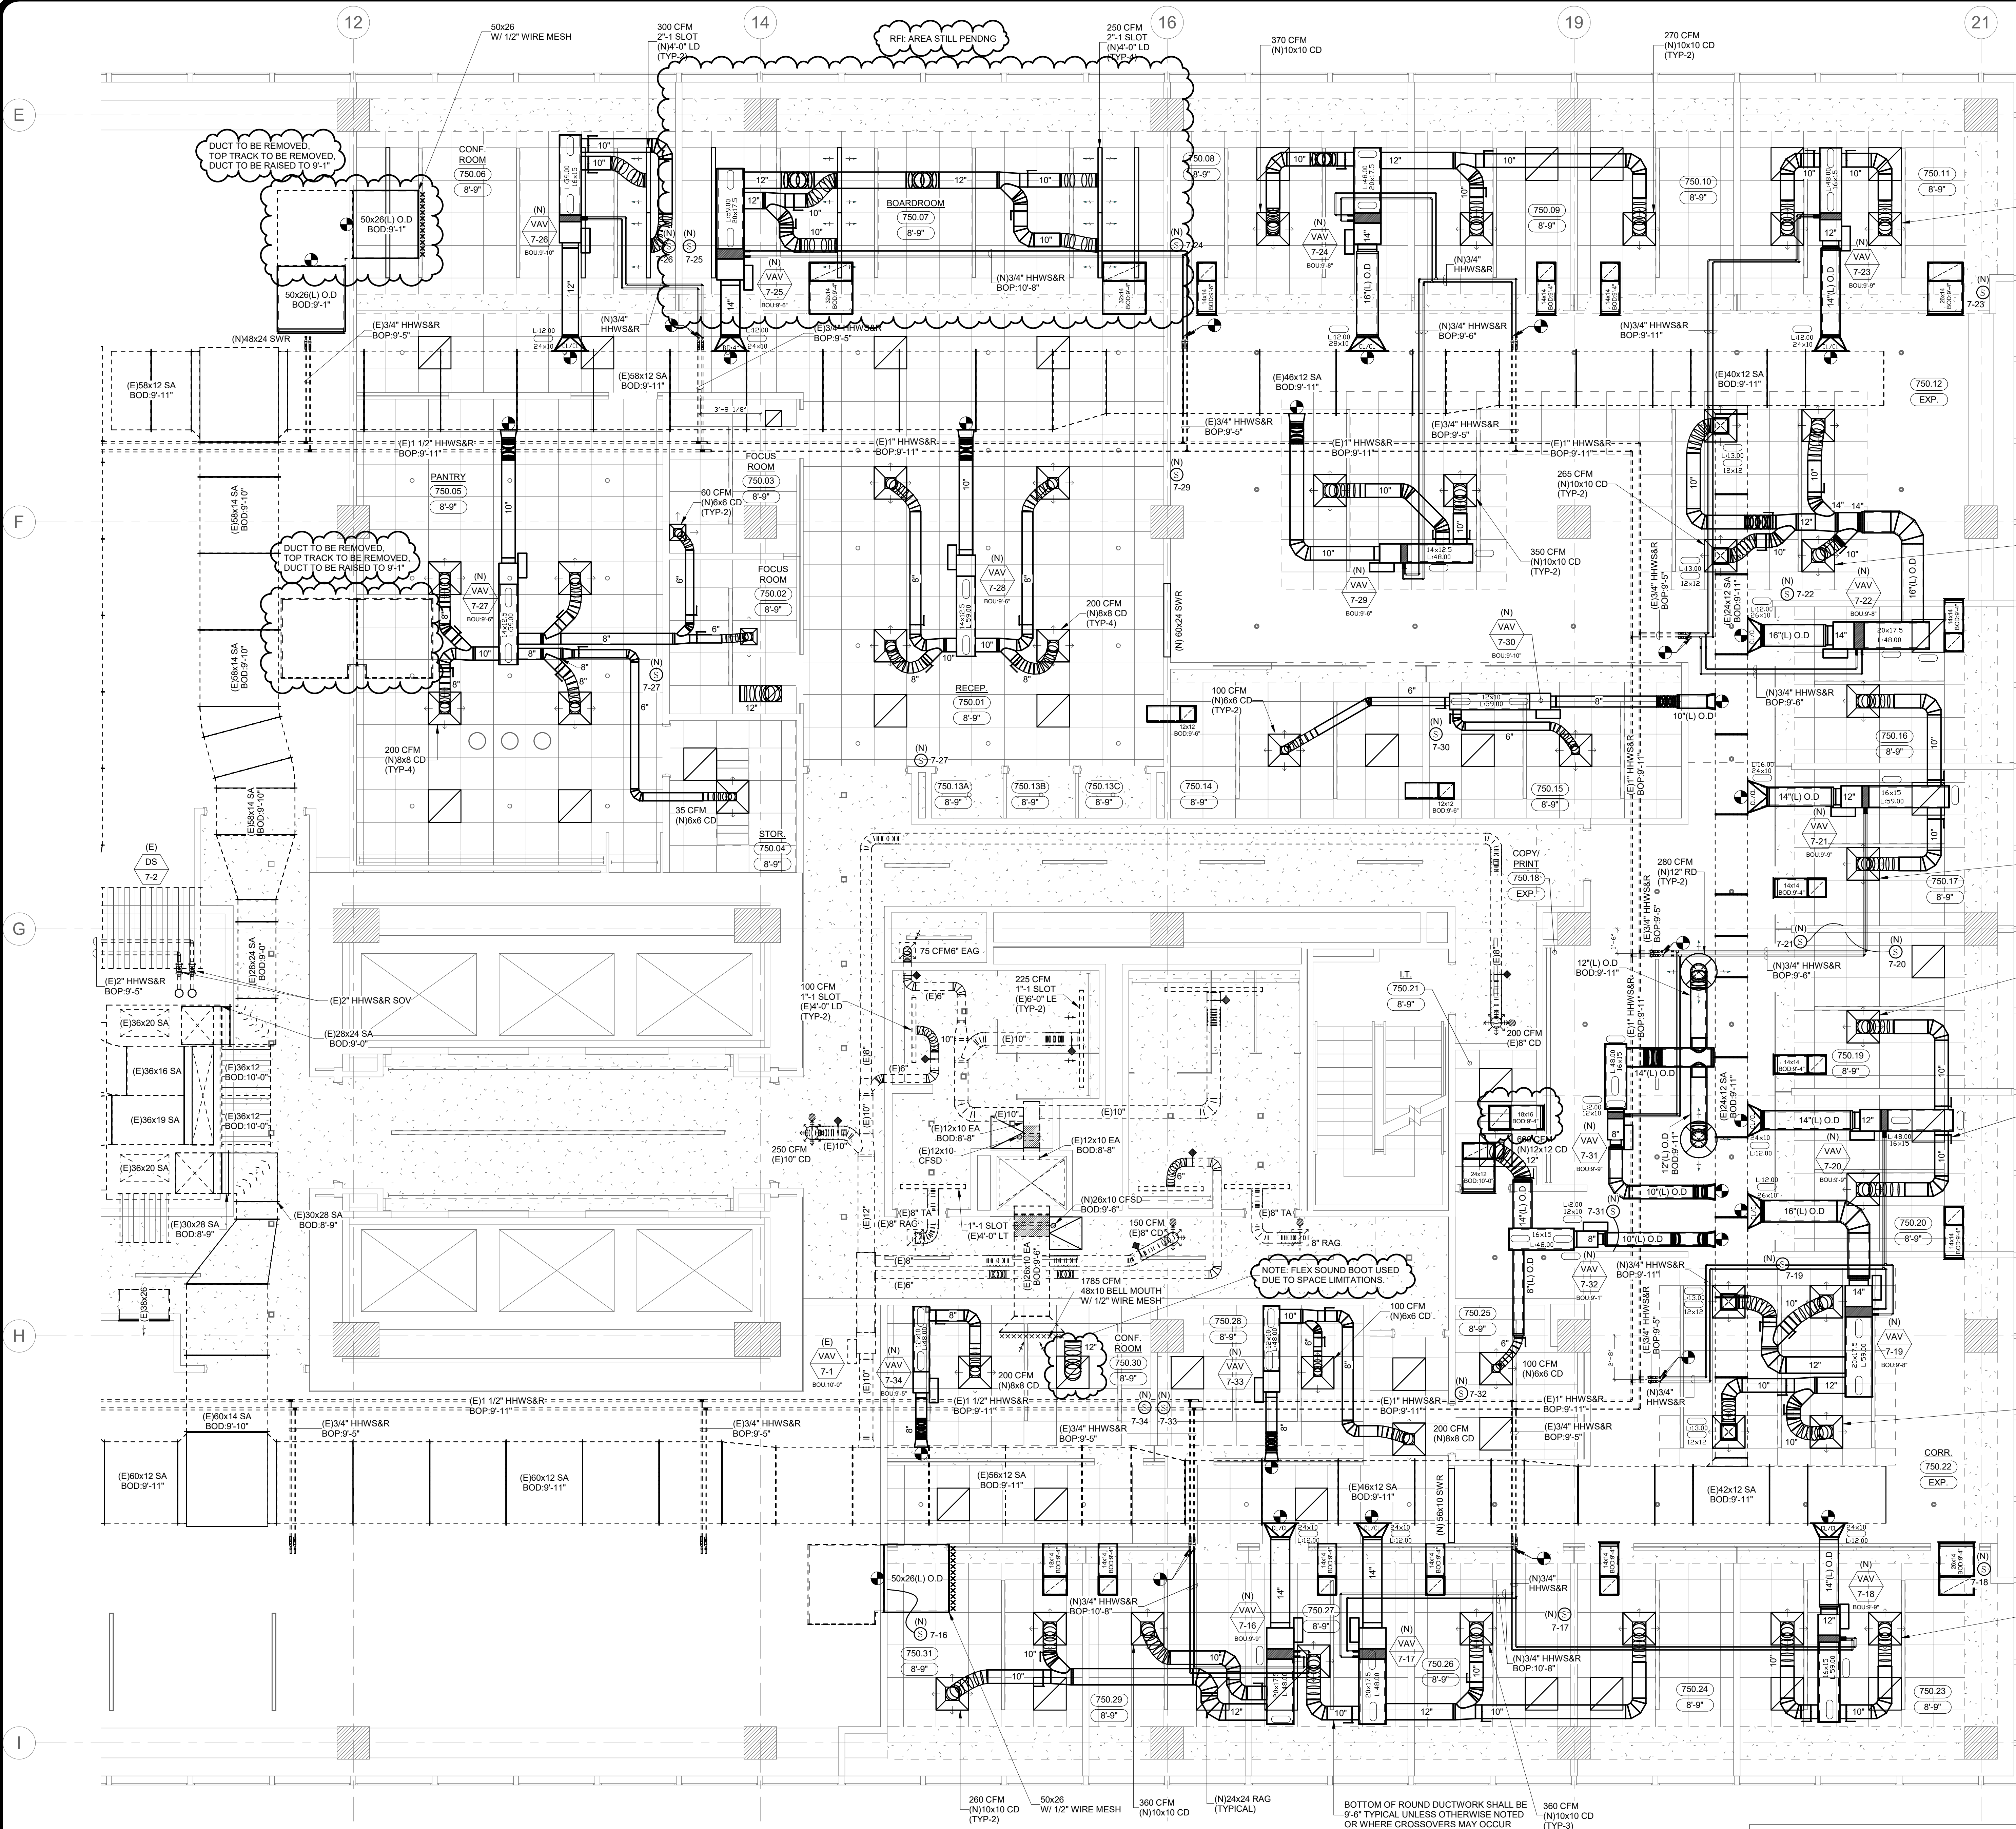


PARTIAL AIR CONDITIONING 7TH FLOOR CONSTRUCTION DRAWING

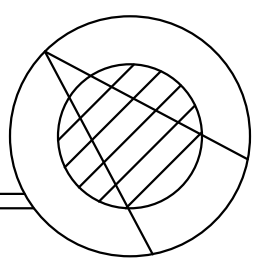

| MECHANICAL LEGEND |                         |  |                           |
|-------------------|-------------------------|--|---------------------------|
|                   | DUCT RISER (SUPPLY)     |  | POINT OF CONNECTION (POC) |
|                   | DUCT RISER (RETURN)     |  | UNDERCUT DOOR             |
|                   | DUCT RISER (EXHAUST)    |  | ROOM THERMOSTAT/ SENSOR   |
|                   | CEILING DIFFUSER (CD)   |  | MECHANICAL CONTRACTOR     |
|                   | EXIST CEILING DIFFUSER  |  | ELECTRICAL CONTRACTOR     |
|                   | RETURN AIR GRILLE       |  | SMOKE DETECTOR            |
|                   | EXIST RETURN AIR GRILLE |  | AIR-TEC                   |
|                   | THERMO-FUSER            |  | FIRE DAMPER (FD)          |
|                   | ACCESS DOOR (AD)        |  | MANUAL VOLUME DAMPER      |
|                   | CENTER LINE             |  | MOTORIZED DAMPER (MD)     |

| ABBREVIATION |                                        |        |                                  |
|--------------|----------------------------------------|--------|----------------------------------|
| AFF          | ABOVE FINISHED FLOOR                   | LRA    | LOCKED ROTOR AMPS                |
| BDD          | BACKDRAFT DAMPER                       | MA     | MAKE-UP AIR                      |
| BI           | BLACK IRON                             | MB     | MIXING BOX                       |
| BOD          | BOTTOM OF DUCT                         | MD     | MIXING DAMPER                    |
| BTUH         | BRITISH THERMAL UNITS/HOUR             | MBH    | THOUSAND BTUS PER HOUR           |
| CB           | CIRCUIT BREAKER                        | MCA    | MINIMUM CIRCUIT AMPACITY         |
| CD           | CEILING DIFFUSER                       | MFS    | MAXIMUM FUSE SIZE                |
| CEU          | CONDENSATE EVAPORATOR UNIT             | N      | NEW DUCT/EQUIPMENT               |
| CFM          | CUBIC FEET PER MINUTE                  | NIC    | NOT IN CONTRACT                  |
| CHWR         | CHILLED WATER RETURN                   | OD     | OUTSIDE DIMENSION                |
| CHWS         | CHILLED WATER SUPPLY                   | OSA    | OUTSIDE AIR                      |
| CI           | CAST IRON                              | PSIG   | POUNDS PER SQUARE INCH GAUGE     |
| COP          | COEFFICIENT OF PERFORMANCE             | PVC    | POLYVINYL CHLORIDE               |
| CU FT        | CUBIC FEET                             | (R)    | RELOCATED DUCT/EQUIPMENT         |
| DB           | DRY BULB (°F)                          | RA     | RETURN AIR                       |
| DTR          | DOWN THRU ROOF                         | RAG    | RETURN AIR GRILLE                |
| (E)          | EXISTING DUCT/EQUIPMENT                | RLA    | RATED LOAD AMPS                  |
| EA           | EXHAUST AIR                            | SA     | SUPPLY AIR                       |
| EAG          | EXHAUST AIR GRILLE                     | SEER   | SEASONAL ENERGY EFFICIENCY RATIO |
| EMD          | ELECTRIC MODULATING DAMPER             | CSFD   | COMBINATION SMOKE/FIRE DAMPER    |
| F            | FAHRENHEIT                             | SP     | STATIC PRESSURE                  |
| FC           | FLEX CONNECTION                        | SWG    | SIDEWALL GRILLE                  |
| FLA          | FULL LOAD AMPS                         | SWR    | SIDEWALL REGISTER                |
| GA           | GAUGE                                  | TD     | TEMPERATURE DIFFERENCE =         |
| GALV         | GALVANIZED                             | TOD    | TOP OF DUCT                      |
| GPM          | GALLONS PER MINUTE                     | UTR    | UP THRU ROOF                     |
| HEPA         | HIGH EFFICIENCY PARTICULATE AIR FILTER | VAV    | VARIABLE AIR VOLUME              |
| HP           | HORSEPOWER                             | VAV.FP | VAV, FAN POWERED                 |
| HWR          | HOT WATER RETURN                       | VD     | VOLUME DAMPER                    |
| HWS          | HOT WATER SUPPLY                       | VENT   | VENTILATING                      |
| ID           | INSIDE DIMENSION                       | VOL    | VOLUME                           |
| IPS          | IRON PIPE SIZE                         | WB     | WET BULB (°F)                    |
| (L)          | LINED DUCT                             | WC     | WATER COLUMN (IN. HG)            |
| LD           | LINEAR DIFFUSER                        | WT(H)  | WEIGHT IN POUNDS                 |

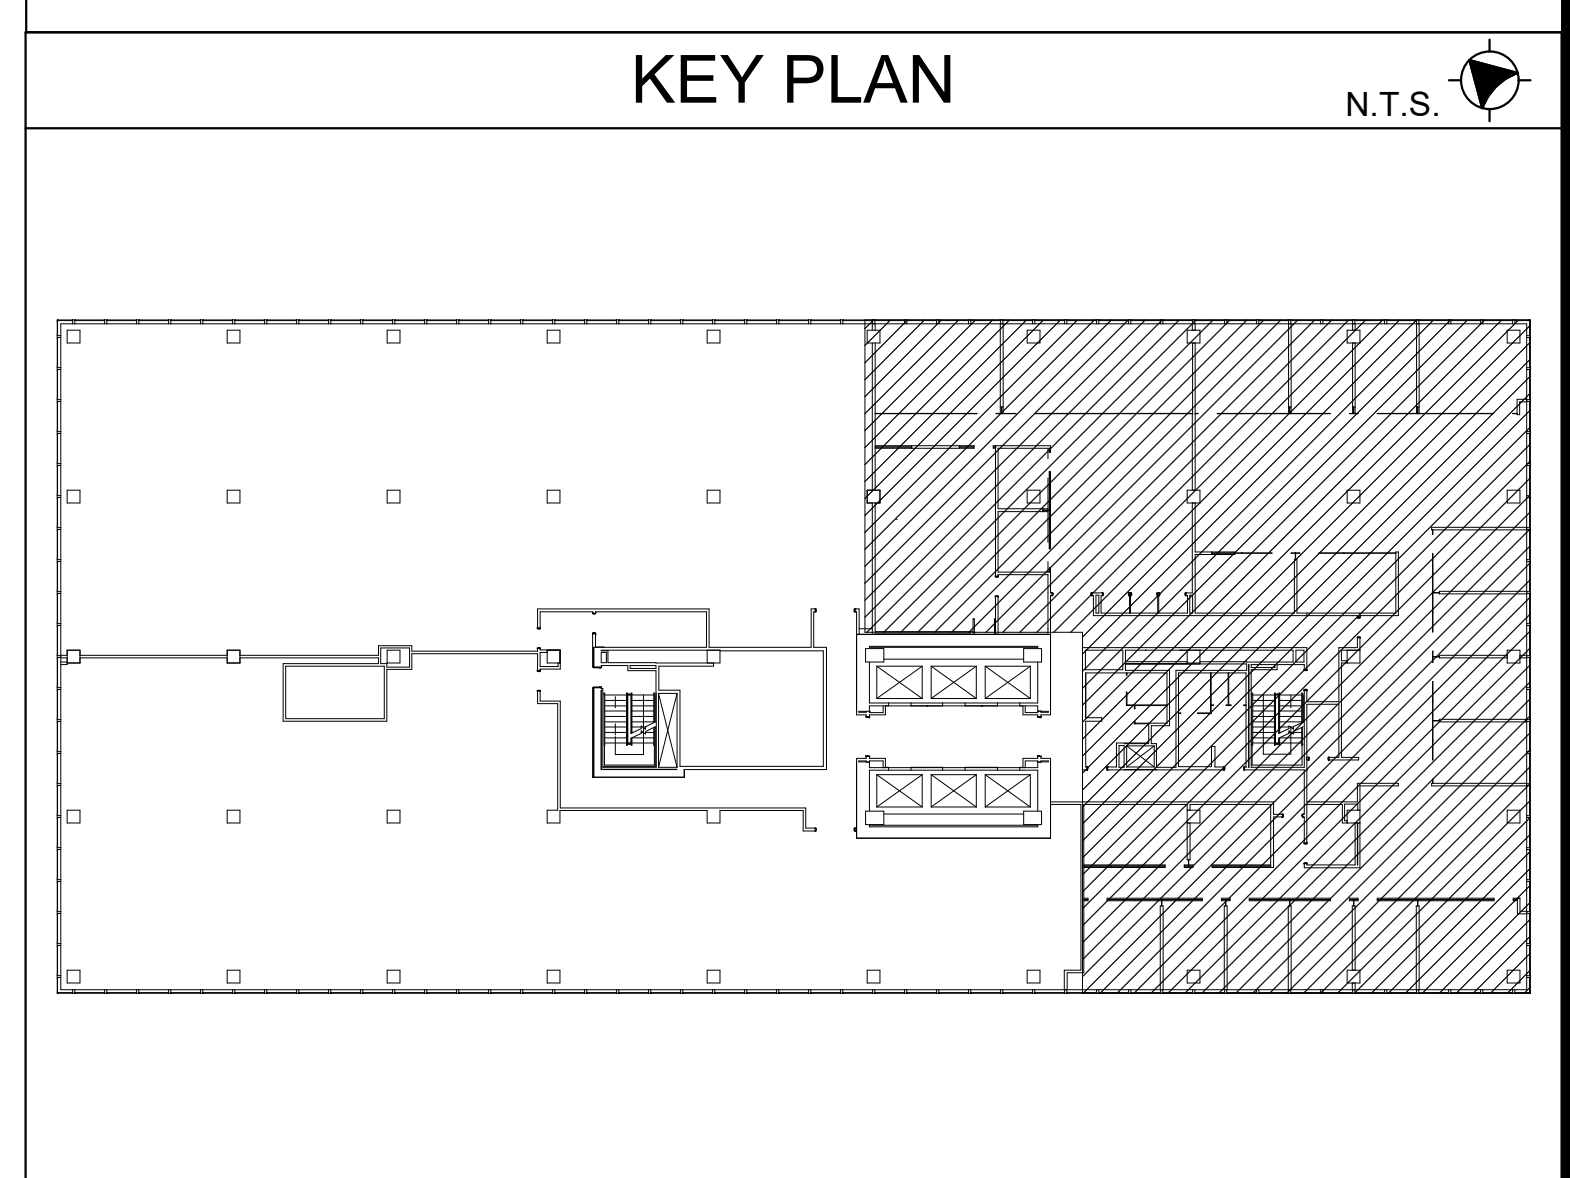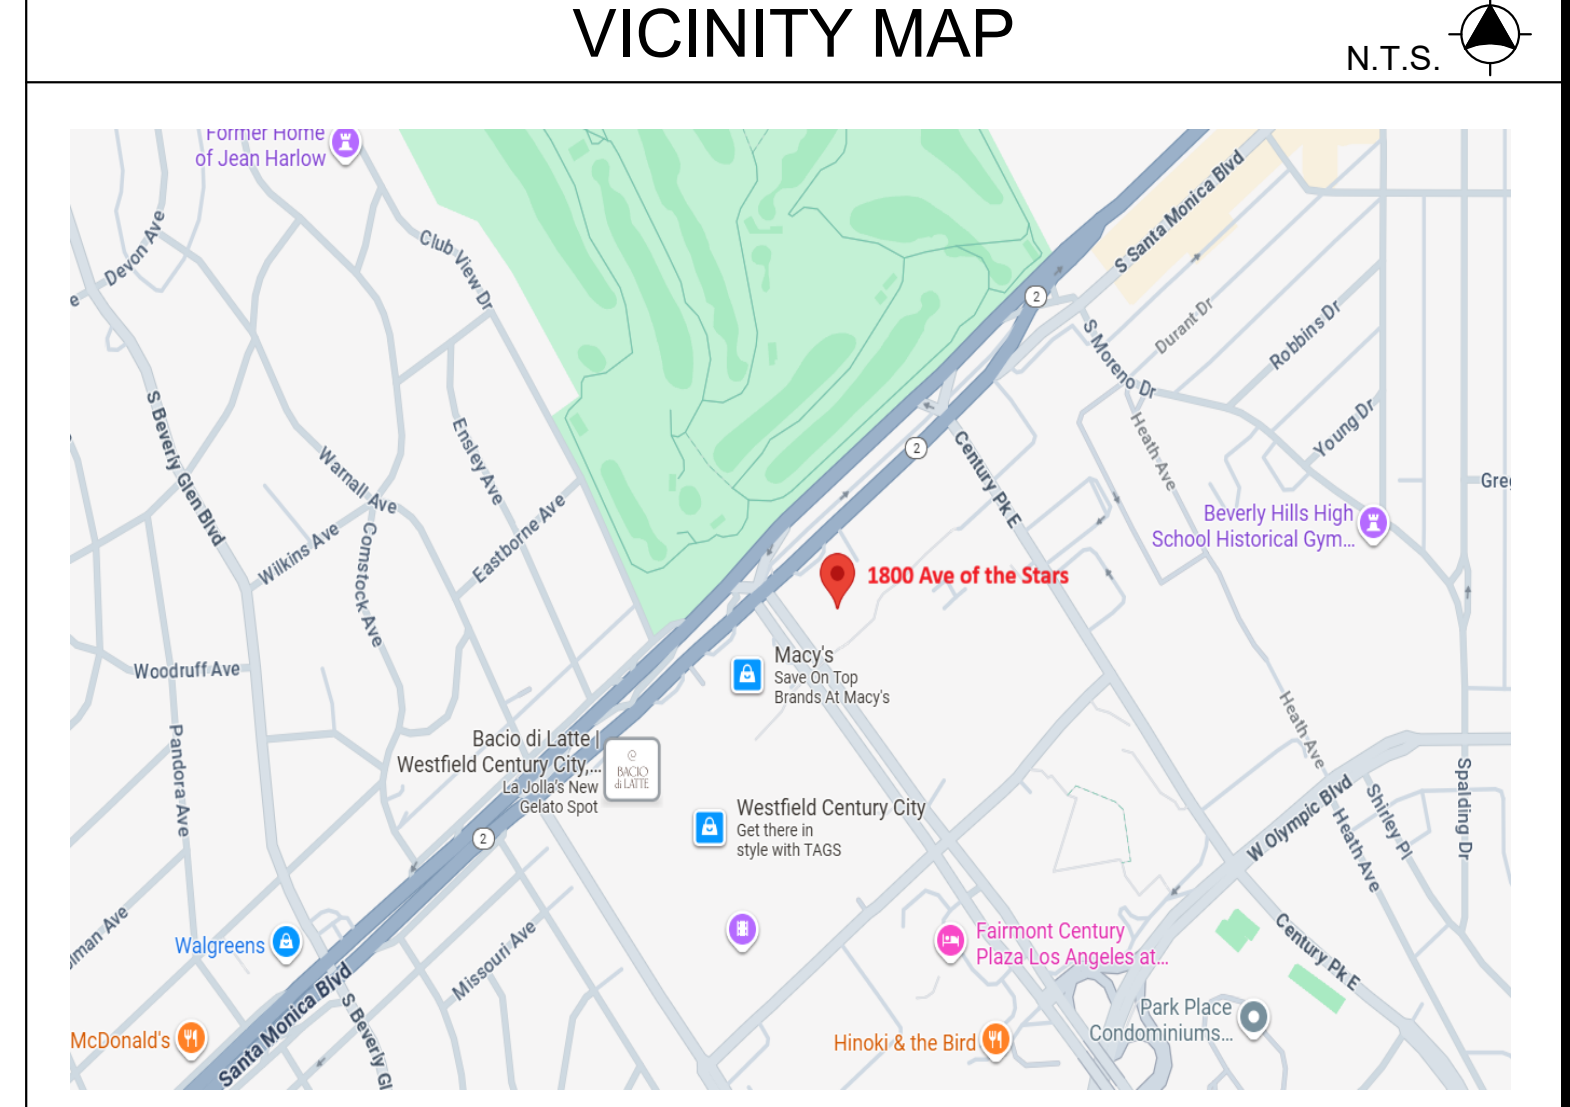

| APPROVAL                | SIGNATURE | DATE     |
|-------------------------|-----------|----------|
| RE-ENGINEERING COMPLETE | TO        | 04-14-26 |
| PROJECT MANAGER         |           |          |
| ENGINEERING             |           |          |
| SHEET METAL FOREMAN     |           |          |
| PIPING OFFICE           |           |          |

| SUITE 750 - VARIABLE AIR VOLUME BOX SCHEDULE |                            |                  |               |              |              |          |             |          |          |       |     |          |          |                               |                         |                    |
|----------------------------------------------|----------------------------|------------------|---------------|--------------|--------------|----------|-------------|----------|----------|-------|-----|----------|----------|-------------------------------|-------------------------|--------------------|
| MARK                                         | MANUFACTURER AND MODEL NO. | INLET SIZE (IN.) | AIRFLOW (CFM) |              |              | ΔP (IN.) | REHEAT COIL |          |          |       |     |          |          | MAX SENSIBLE CAPACITY (BTU/h) | OPERATING WEIGHT (LBS.) | REMARKS            |
|                                              |                            |                  | COOLING MAX.  | COOLING MIN. | HEATING MAX. |          | AIR         |          |          | WATER |     |          |          |                               |                         |                    |
|                                              |                            |                  |               |              |              |          | EDB (°F)    | LDB (°F) | ΔP (IN.) | GPM   | ROW | EWT (°F) | ΔP (IN.) |                               |                         |                    |
| VAV-7-1                                      | TITUS/ DESV                | 10"              | 800           | 0            | --           | 8.000    | --          | --       | --       | --    | --  | --       | --       | --                            | --                      | EXISTING TO REMAIN |
| VAV-7-16                                     | TITUS/ DESV                | 14"              | 880           | 300          | 440          | 0.039    | 55          | 94       | 0.15     | 2.4   | 2   | 180      | 0.75     | 48000                         | 90                      | NEW/ BALANCE       |
| VAV-7-17                                     | TITUS/ DESV                | 14"              | 1080          | 324          | 540          | 0.039    | 55          | 94       | 0.15     | 2.4   | 2   | 180      | 0.75     | 48000                         | 90                      | NEW/ BALANCE       |
| VAV-7-18                                     | TITUS/ DESV                | 12"              | 720           | 216          | 360          | 0.031    | 55          | 101      | 0.15     | 1.9   | 2   | 180      | 0.55     | 37200                         | 75                      | NEW/ BALANCE       |
| VAV-7-19                                     | TITUS/ DESV                | 14"              | 1060          | 318          | 530          | 0.039    | 55          | 94       | 0.15     | 2.4   | 2   | 180      | 0.75     | 48000                         | 90                      | NEW/ BALANCE       |
| VAV-7-20                                     | TITUS/ DESV                | 12"              | 720           | 216          | 360          | 0.031    | 55          | 101      | 0.15     | 1.9   | 2   | 180      | 0.55     | 37200                         | 75                      | NEW/ BALANCE       |
| VAV-7-21                                     | TITUS/ DESV                | 12"              | 720           | 216          | 360          | 0.031    | 55          | 101      | 0.15     | 1.9   | 2   | 180      | 0.55     | 37200                         | 75                      | NEW/ BALANCE       |
| VAV-7-22                                     | TITUS/ DESV                | 14"              | 1060          | 318          | 530          | 0.039    | 55          | 94       | 0.15     | 2.4   | 2   | 180      | 0.75     | 48000                         | 90                      | NEW/ BALANCE       |
| VAV-7-23                                     | TITUS/ DESV                | 12"              | 600           | 190          | 300          | 0.031    | 55          | 101      | 0.15     | 1.9   | 2   | 180      | 0.55     | 37200                         | 75                      | NEW/ BALANCE       |
| VAV-7-24                                     | TITUS/ DESV                | 14"              | 910           | 300          | 455          | 0.039    | 55          | 94       | 0.15     | 2.4   | 2   | 180      | 0.75     | 48000                         | 90                      | NEW/ BALANCE       |
| VAV-7-25                                     | TITUS/ DESV                | 14"              | 1000          | 300          | 500          | 0.039    | 55          | 94       | 0.15     | 2.4   | 2   | 180      | 0.75     | 48000                         | 90                      | NEW/ BALANCE       |
| VAV-7-26                                     | TITUS/ DESV                | 12"              | 600           | 190          | 300          | 0.031    | 55          | 101      | 0.15     | 1.9   | 2   | 180      | 0.55     | 37200                         | 75                      | NEW/ BALANCE       |
| VAV-7-27                                     | TITUS/ DESV                | 10"              | 955           | 287          | --           | --       | --          | --       | --       | --    | --  | --       | --       | --                            | 55                      | NEW/ BALANCE       |
| VAV-7-28                                     | TITUS/ DESV                | 10"              | 800           | 240          | --           | --       | --          | --       | --       | --    | --  | --       | --       | --                            | 55                      | NEW/ BALANCE       |
| VAV-7-29                                     | TITUS/ DESV                | 10"              | 700           | 210          | 350          | 0.090    | 55          | 77       | 0.15     | 2.0   | 1   | 180      | 0.41     | 21300                         | 65                      | NEW/ BALANCE       |
| VAV-7-30                                     | TITUS/ DESV                | 8"               | 200           | 60           | --           | --       | --          | --       | --       | --    | --  | --       | --       | --                            | 45                      | NEW/ BALANCE       |
| VAV-7-31                                     | TITUS/ DESV                | 8"               | 560           | 168          | 280          | 0.110    | 55          | 77       | 0.15     | 1.0   | 1   | 180      | 0.64     | 14000                         | 55                      | NEW/ BALANCE       |
| VAV-7-32                                     | TITUS/ DESV                | 8"               | 700           | 210          | --           | --       | --          | --       | --       | --    | --  | --       | --       | --                            | 45                      | NEW/ BALANCE       |
| VAV-7-33                                     | TITUS/ DESV                | 8"               | 300           | 90           | --           | --       | --          | --       | --       | --    | --  | --       | --       | --                            | 55                      | NEW/ BALANCE       |
| VAV-7-34                                     | TITUS/ DESV                | 8"               | 200           | 60           | --           | --       | --          | --       | --       | --    | --  | --       | --       | --                            | 45                      | NEW/ BALANCE       |

DESCRIPTION

ISSUED FOR APPROVAL

ISSUED FOR RECORD ONLY

DATE

COMPLETED BY

RC

RC

04-08-26

04-15-26

AIR CONDITIONING CONTRACTORS

AIR-TEC

at

CERITY-SUITE 750

7TH FLOOR

1800 AVENUE OF THE STARS

LOS ANGELES, CALIFORNIA

PROJECT CHIEF

HU

DRAWN BY

HUIDUSOTO

CHECKED BY

TO

DATE

04-14-26

SCALE

1/4" = 1'-0"

SHEET

1

OF 1

SHEETS